
ĐỒ ÁN TỐT NGHIỆP KỸ SƯ CƠ SỞ HẠ TẦNG ĐÔ THỊ KHÓA KD20

XÃ MỸ TRÀ - THÀNH PHỐ CAO LÃNH - TỈNH ĐỒNG THÁP


QUY HOẠCH HỆ THỐNG HẠ TẦNG KỸ THUẬT TỶ LỆ 1/2000 KHU DÂN CƯ RẠCH CHANH


BẢN ĐỒ QUY HOẠCH CHUẨN BỊ KỸ THUẬT

SƠ ĐỒ VỊ TRÍ KHU ĐẤT QUY HOẠCH

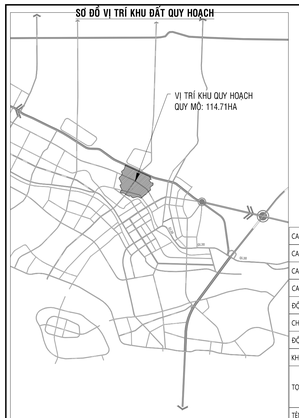

TRẮC DỌC TUYẾN CỐNG THOÁT NƯỚC MƯA ĐIỂN HÌNH TỪ HG1.3 - HG1.5

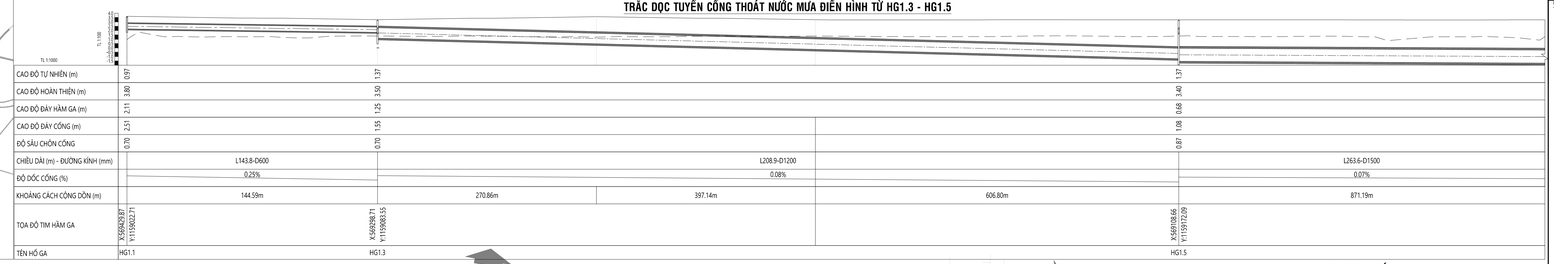

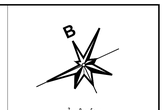

KÍ HIỆU

i=0.30% L=175.85M	ĐỘ DỐC DỌC (%) CHIỀU DÀI DỐC (M)
HG1.3 1.55 3.45	TÊN HỐ GA CAO ĐỘ ĐÁY CỐNG (M) CAO ĐỘ XÂY DỰNG (M)
3.20 / 2.00	CAO ĐỘ THIẾT KẾ (M) CAO ĐỘ TỰ NHIÊN (M)
	CỐNG THOÁT NƯỚC MƯA HIỆN HỮU
	CỐNG THOÁT NƯỚC MƯA QUY HOẠCH
	ĐƯỜNG PHÂN CHIA LƯU VỰC
L155-D1000-i0,18%	CHIỀU DÀI(M)- ĐƯỜNG KÍNH(MM)- ĐỘ DỐC(%) HƯỚNG DỐC CỐNG
	HỐ GA
	CỬA XẢ
1 1	KÍ HIỆU MẶT CẮT
S H W	S: DIỆN TÍCH (HA) H: CHIỀU CAO (M) W: KHỐI LƯỢNG (M^3)

CHÚ THÍCH TRẮC DỌC

	ĐƯỜNG THIẾT KẾ
	ĐƯỜNG TỰ NHIÊN

BẢNG TỔNG HỢP KHỐI LƯỢNG THOÁT NƯỚC MƯA

STT	HẠNG MỤC	ĐƠN VỊ	KHỐI LƯỢNG
	HẠNG MỤC ĐÀO ĐẮP		
1	**DIỆN TÍCH ĐÀO ĐẮP**		
1.1	DIỆN TÍCH ĐẮT ĐẮP	M^2	1061562.00
1.2	DIỆN TÍCH ĐẤT ĐÀO	M^2	-
1.3	DIỆN TÍCH KHÔNG ĐÀO ĐẮP	M^2	85532.00
2	**KHỐI LƯỢNG ĐẤT ĐÀO ĐẮP**		
2.1	KHỐI LƯỢNG ĐẤT ĐẮP	M^3	1830813.76
2.2	KHỐI LƯỢNG ĐẤT ĐÀO	M^3	-
2.3	KHỐI LƯỢNG ĐẤT BỘC HỮU CƠ (H = 0.3M)	M^3	318468.648
2.4	KHỐI LƯỢNG ĐẤT BỘ HỮU CƠ (H = 0.3M)	M^3	318468.648
3	**TỔNG KHỐI LƯỢNG ĐẤT ĐÀO (2.2+2.3)**	M^3	318468.648
4	**TỔNG KHỐI LƯỢNG ĐẤT ĐẮP (2.1+2.4)**	M^3	2149281.648

BẢNG TỔNG HỢP KHỐI LƯỢNG THOÁT NƯỚC MƯA

STT	HẠNG MỤC	ĐƠN VỊ	KHỐI LƯỢNG
I	**CỐNG TRÒN BTCT THOÁT NƯỚC MƯA**	M	17064.30
1.1	CỐNG D600	M	3866.41
1.2	CỐNG D800	M	5427.66
1.3	CỐNG D1000	M	3516.83
1.4	CỐNG D1200	M	2354.76
1.5	CỐNG D1500	M	1898.61
II	**CỬA XẢ**		19
2.1	CỬA XẢ D600	CÁI	3
2.2	CỬA XẢ D800	CÁI	8
2.3	CỬA XẢ D1000	CÁI	7
2.4	CỬA XẢ D1200	CÁI	1
III	**HỐ GA**	HỐ	159

THUYẾT MINH SƠ BỘ

1. CƠ SỞ THIẾT KẾ :

- QCXDVN: 01: 2021/ BXD QUY CHUẨN XÂY DỰNG VIỆT NAM VỀ QUY HOẠCH XÂY DỰNG.
- QCXDVN: 07-2: 2023/ BXD QUY CHUẨN KỸ THUẬT QUỐC GIA CÁC CÔNG TRÌNH HẠ TẦNG KỸ THUẬT - CÔNG TRÌNH THOÁT NƯỚC.
- TCVN 7957-2023 THOÁT NƯỚC-MẠNG LƯỚI BÊN NGOÀI VÀ CÔNG TRÌNH.
- BẢN ĐỒ QUY HOẠCH TỔNG MẶT BẰNG SỬ DỤNG ĐẤT TỶ LỆ 1/2000.
- CĂN CỨ TÀI LIỆU THỦY VĂN KHU VỰC XÂY DỰNG CÔNG TRÌNH.
- CÁC TÀI LIỆU KHÁC VÀ CÁC QUY TRÌNH HIỆN HÀNH KHÁC LIÊN QUAN

2. GIẢI PHÁP QUY HOẠCH:


A. QUY HOẠCH CAO ĐỘ NỀN:

- CAO ĐỘ SAN NỀN TÍNH ĐẾN TIM ĐƯỜNG H_{tim} 3.20 M.
- KHỐI LƯỢNG SAN LẤP TÍNH CHO TOÀN KHU LÀ +1830813.76 M^3.

B. THOÁT NƯỚC MẶT:

- GIẢI PHÁP THOÁT NƯỚC MƯA CHO KHU DỰ ÁN LÀ THIẾT KẾ HỆ THỐNG THOÁT NƯỚC MƯA RIÊNG VỚI NƯỚC THẢI SINH HOẠT. NƯỚC MƯA TRÊN TOÀN BỘ BỀ MẶT KHU VỰC THIẾT KẾ SẼ ĐƯỢC GOM VỀ CÁC TUYẾN CỐNG THOÁT NƯỚC DỌC THEO CÁC TRỤC GIAO THÔNG SAU ĐÓ XẢ RA RẠCH CHANH, RẠCH BÀ VẠI, SÔNG SAO CÁI THƯỢNG.
- CỐNG THOÁT NƯỚC MƯA SỬ DỤNG CỐNG TRÒN BTCT CÓ KHẢ NĂNG CHỊU LỰC, KÍCH THƯỚC CỐNG TỪ CỐNG TRÒN D600MM ĐẾN D1500MM.
- TRONG CÁC LƯU VỰC CHÍNH SẼ CHIA THÀNH CÁC LƯU VỰC THOÁT NƯỚC NHỎ NHẰM MỤC ĐÍCH THU GOM 100% LƯỢNG NƯỚC MẶT TỪ NƠI PHÁT SINH RA NGUỒN TIẾP NHẬN MỘT CÁCH NHANH NHẤT.
- ĐỘ DỐC ĐẶT CỐNG: TRÊN CƠ SỞ BÁM SÁT ĐỘ DỐC ĐỊA HÌNH THIẾT KẾ TUY NHIÊN VẪN PHẢI ĐẢM BẢO ĐỘ DỐC CỐNG TỐI THIỂU I/D.
- QUY TRÌNH TÍNH TOÁN THỦY LỰC TUÂN THEO TIÊU CHUẨN 7957:2023


MẶT CẮT GIAO THÔNG ĐIỂN HÌNH

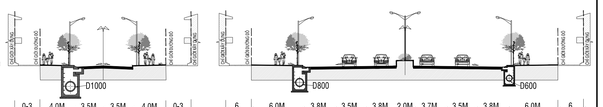

MẶT CẮT 2-2 TỶ LỆ 1/200

MẶT CẮT 1-1 TỶ LỆ 1/200

SƠ ĐỒ PHÂN CHIA LƯU VỰC THOÁT NƯỚC MƯA

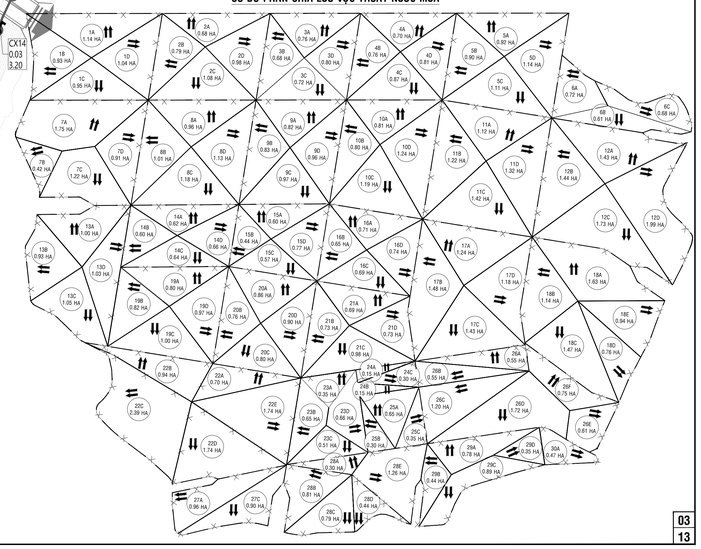

CHÚ THÍCH:

- RANH GIỚI QUY HOẠCH
- ĐẤT Ở XÓM LÀNG HIỆN HỮU
- ĐẤT NHÓM NHÀ Ở HIỆN HỮU
- ĐẤT NHÓM NHÀ Ở MỚI
- ĐẤT Y TẾ
- ĐẤT TRƯỜNG THPT
- ĐẤT TRƯỜNG THCS, TIỂU HỌC MẦM NON
- ĐẤT THỂ DỤC THỂ THAO
- ĐẤT CÂY XANH SỬ DỤNG CÔNG CỘNG
- ĐẤT CÂY XANH CHUYÊN DỤNG
- ĐẤT CƠ QUAN, TRỤ SỞ
- ĐẤT THƯƠNG MẠI
- ĐẤT DỊCH VỤ
- ĐẤT BÃI ĐỖ XE ĐỐ THỊ
- ĐẤT HẠ TẦNG KỸ THUẬT KHÁC
- ĐẤT SÔNG SUỐI, KÊNH RẠCH