
ĐỒ ÁN TỐT NGHIỆP KỸ SƯ CƠ SỞ HẠ TẦNG ĐÔ THỊ KHÓA KD20

XÃ MỸ TRÀ - THÀNH PHỐ CAO LÃNH - TỈNH ĐỒNG THÁP


QUY HOẠCH HỆ THỐNG HẠ TẦNG KỸ THUẬT TỶ LỆ 1/2000 KHU DÂN CƯ RẠCH CHANH

BẢN ĐỒ QUY HOẠCH HỆ THỐNG CẤP NƯỚC

SƠ ĐỒ LIÊN HỆ VỊ TRÍ KHU ĐẤT QUY HOẠCH VÀ ĐẤU MỐI HẠ TẦNG KĨ THUẬT

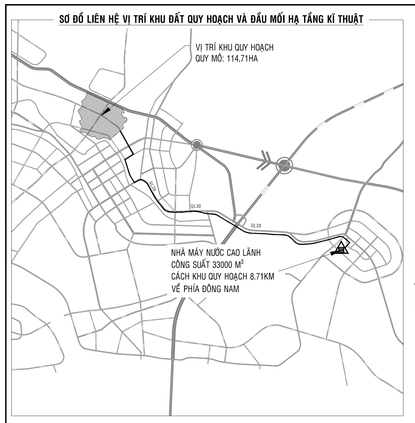

MẶT CẮT GIAO THÔNG ĐIỂN HÌNH

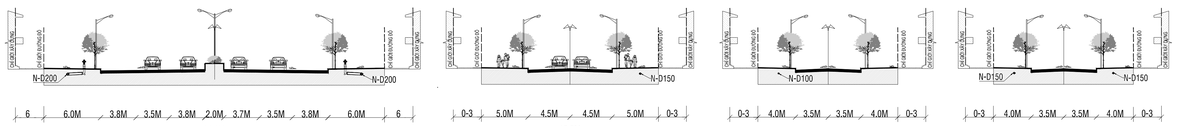

MẶT CẮT 1-1
TỶ LỆ 1/200

MẶT CẮT 2-2
TỶ LỆ 1/200

MẶT CẮT 3-3
TỶ LỆ 1/200

MẶT CẮT 4-4
TỶ LỆ 1/200

KÍ HIỆU

- ĐƯỜNG ỐNG CẤP NƯỚC QUY HOẠCH
- ĐƯỜNG ỐNG CẤP NƯỚC HIỆN HỮU
- D150-L705 — ĐƯỜNG KÍNH (MM) - CHIỀU DÀI (M)
- TRỤ CHỮA CHÁY
- KÍ HIỆU MẶT CẮT
- D200 - L761 — ĐƯỜNG KÍNH ỐNG (MM)
- q6.9 - v1.38 — CHIỀU DÀI ĐOẠN ỐNG (M)
- h0.24 — VẬN TỐC ĐOẠN ỐNG (M/S)
- TỔN THẤT (M)
- LƯU LƯỢNG ĐOẠN ỐNG (L/S)
- LƯU LƯỢNG TẬP TRUNG (L/S)
- LƯU LƯỢNG SINH HOẠT (L/S)
- LƯU LƯỢNG CHỮA CHÁY (L/S)
- TÊN NÚT

THUYẾT MINH SƠ BỘ

I. CƠ SỞ THIẾT KẾ:

- QCVN 01:2021/BXD QUY CHUẨN KỸ THUẬT QUỐC GIA VỀ QUY HOẠCH XÂY DỰNG.
- QCVN 06:2020/BXD QUY CHUẨN KỸ THUẬT QUỐC GIA VỀ AN TOÀN CHÁY CHO NHÀ VÀ CÔNG TRÌNH.
- QCVN 07-01:2023/BXD QUY CHUẨN KỸ THUẬT QUỐC GIA VỀ HỆ THỐNG CÁC CÔNG TRÌNH HẠ TẦNG KỸ THUẬT - CÔNG TRÌNH CẤP NƯỚC.
- TCVN 13606:2023 CẤP NƯỚC - MẠNG LƯỚI ĐƯỜNG ỐNG VÀ CÔNG TRÌNH -YÊU CẦU THIẾT KẾ.
- TT 04:2022/BXD QUY ĐỊNH VỀ HỒ SƠ NHIỆM VỤ VÀ HỒ SƠ ĐỒ ÁN QUY HOẠCH XÂY DỰNG VÙNG LIÊN HUYỆN. QUY HOẠCH XÂY DỰNG VÙNG HUYỆN, QUY HOẠCH ĐÔ THỊ, QUY HOẠCH XÂY DỰNG KHU CHỨC NĂNG VÀ QUY HOẠCH NÔNG THÔN.

II. TIÊU CHUẨN CẤP NƯỚC QUY HOẠCH:

- TIÊU CHUẨN DÙNG NƯỚC SINH HOẠT: 130 L/NGƯỜI/NGÀY VỚI 100% DÂN SỐ ĐƯỢC CẤP NƯỚC.
- TỔNG NHU CẦU DÙNG NƯỚC KHOẢNG 5066 M^3/NGÀY ĐÊM.

III. QUY HOẠCH MẠNG LƯỚI CẤP NƯỚC:


- GIỮ NGUYÊN CÁC TUYẾN ỐNG CẤP NƯỚC HIỆN TRẠNG ĐANG CÓ TRONG KHU VỰC, THAY THẾ CẢI TẠO MỘT SỐ ĐOẠN BỊ ẢNH HƯỞNG HẾT NIÊN HẠN SỬ DỤNG CÙNG NHƯ KHÔNG ĐẢM BẢO VỀ ĐÁP ỨNG LƯU LƯỢNG VÀ ÁP LỰC CHO QUÁ TRÌNH PHÁT TRIỂN MỚI NHƯ NẰM TRÊN CÁC TRỤC ĐƯỜNG NHƯ LÊ DUẨN, TRẦN THỊ CÁNH, NGUYỄN HỮU NGHĨA,...
- BỔ SUNG XÂY MỚI CÁC TUYẾN ỐNG ĐỂ ĐẢM BẢO CUNG CẤP 100% CHO CÁC NHU CẦU DÙNG NƯỚC CỦA KHU VỰC CŨNG NHƯ LIÊN KẾT VỚI CÁC KHU VỰC KHÁC TRÊN TOÀN THÀNH PHỐ CAO LÃNH.
- CÁC TUYẾN ỐNG CẤP NƯỚC VỚI ĐƯỜNG KÍNH TỪ D100 - D300 KẾT NỐI VỚI CÁC TUYẾN ỐNG CẤP NƯỚC HIỆN TRẠNG VÀ ĐÃ ĐỊNH HƯỚNG THEO QUY HOẠCH CHUNG CỦA THÀNH PHỐ TẠO THÀNH MẠNG VÒNG KHÉP KÍN ĐẢM BẢO AN TOÀN CẤP NƯỚC CHO CÁC KHU CHỨC NĂNG CỦA KHU VỰC QUY HOẠCH. SỬ DỤNG ỐNG HDPE SẢN XUẤT PHÙ HỢP VỚI TIÊU CHUẨN ISO 4422:1990, ÁP SUẤT PN ≥ 10 CHO MẠNG LƯỚI ỐNG TRONG KHU VỰC.
- HỆ THỐNG CẤP NƯỚC ĐƯỢC ĐẶT TRONG HÀO KỸ THUẬT CHÔN TRÊN VỈA HÈ VÀ CÁCH TƯỜNG CÔNG TRÌNH 1.0M.

IV. HỆ THỐNG CẤP NƯỚC CHỮA CHÁY:

- LƯU LƯỢNG CẤP NƯỚC CHỮA CHÁY 15(L/S), SỐ ĐÁM CHÁY 2, THỜI GIAN 3 GIỜ.
- DỰA VÀO HỆ THỐNG CẤP NƯỚC CHÍNH CỦA KHU QUY HOẠCH BỐ TRÍ MỚI VÀ BỔ SUNG CÁC HỌNG LẤY NƯỚC CHỮA CHÁY D100 ĐẢM BẢO KHOẢNG CÁCH 150M CŨNG NHƯ CÁC TUYẾN ĐƯỜNG NHÁNH. NGOÀI RA KHI CÓ SỰ CỐ CHÁY CẦN BỔ SUNG THÊM NGUỒN NƯỚC MẶT CỦA SÔNG VÀ KÊNH RẠCH GẦN NHẤT ĐỂ CHỮA CHÁY.

BẢNG TỔNG HỢP KHỐI LƯỢNG CẤP NƯỚC


STT	HẠNG MỤC	ĐƠN VỊ	KHỐI LƯỢNG
I	ỐNG CẤP NƯỚC HDPE	M	11537.94
1.1	ỐNG D100	M	2939.01
1.2	ỐNG D150	M	4299.68
1.3	ỐNG D200	M	2395.52
1.4	ỐNG D300	M	1903.73
II	TRỤ CỨU HỎA	TRỤ	59

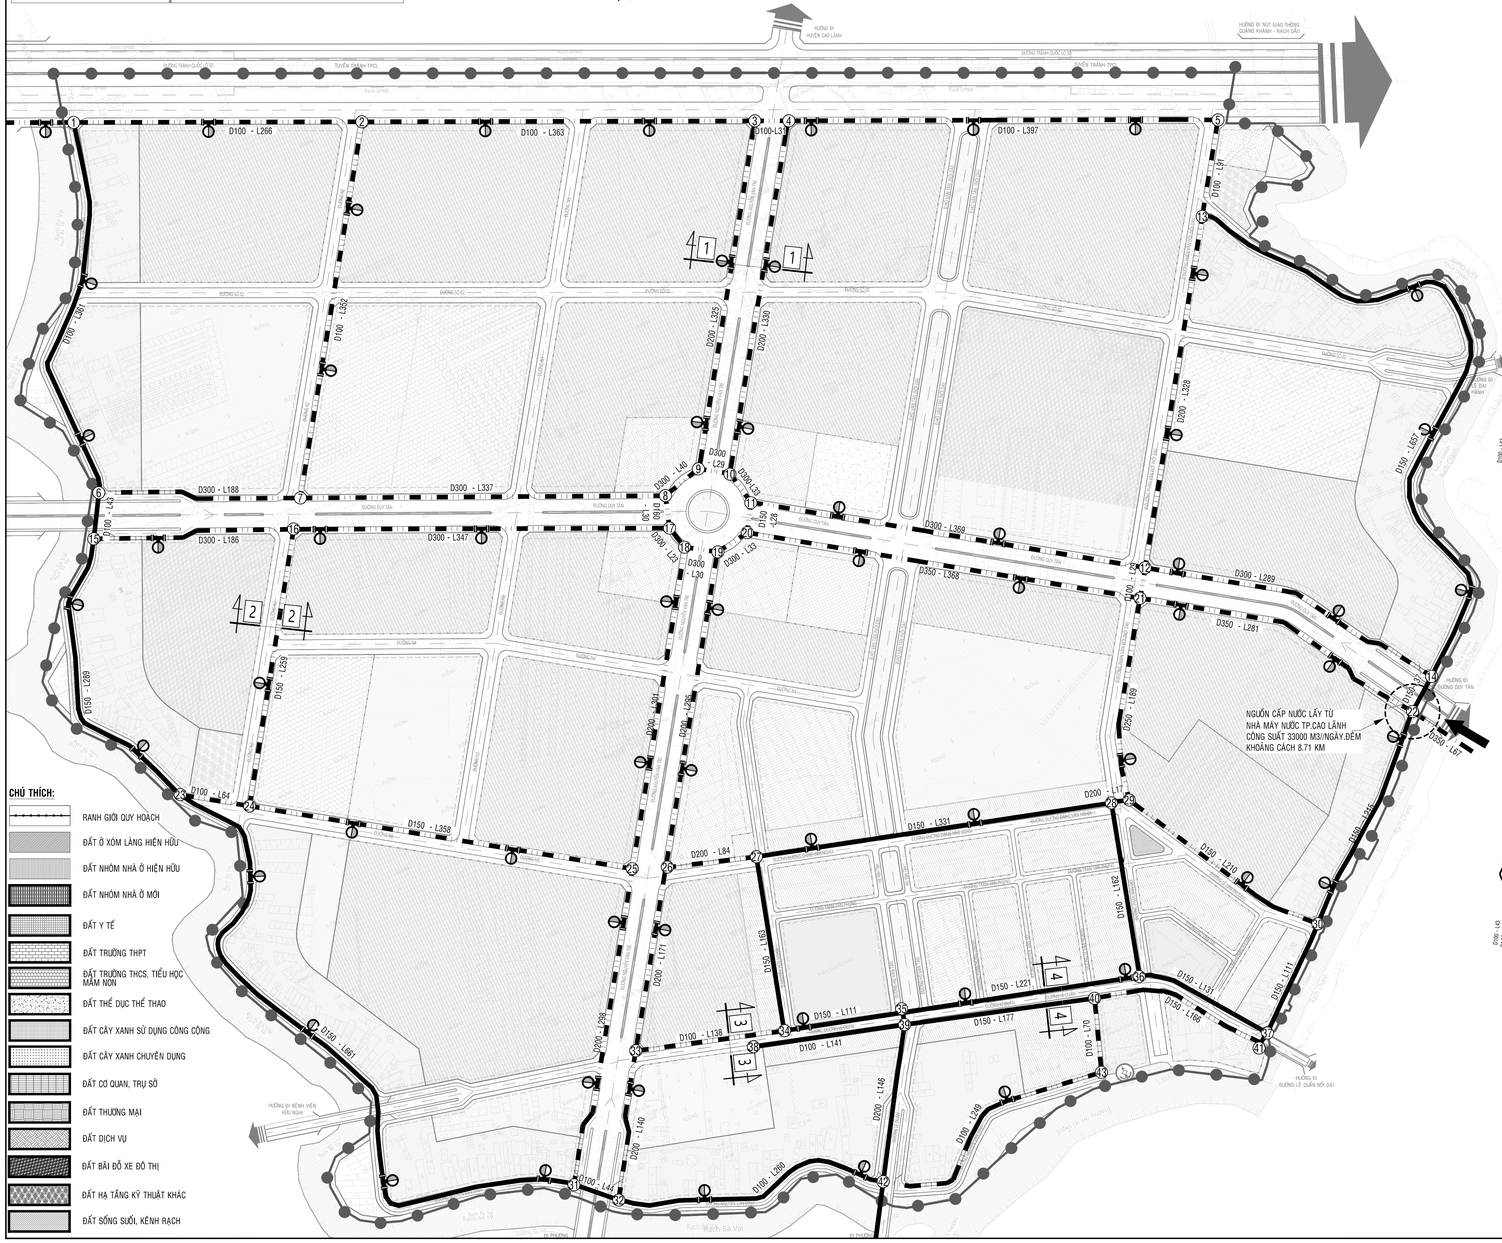

CHÚ THÍCH:

- RANH GIỚI QUY HOẠCH
- ĐẤT Ở XÓM LÀNG HIỆN HỮU
- ĐẤT NHÓM NHÀ Ở HIỆN HỮU
- ĐẤT NHÓM NHÀ Ở MỚI
- ĐẤT Y TẾ
- ĐẤT TRƯỜNG THPT
- ĐẤT TRƯỜNG THCS, TIỂU HỌC MẦM NON
- ĐẤT THỂ DỤC THỂ THAO
- ĐẤT CÂY XANH SỬ DỤNG CÔNG CỘNG
- ĐẤT CÂY XANH CHUYÊN DỤNG
- ĐẤT CƠ QUAN, TRỤ SỞ
- ĐẤT THƯƠNG MẠI
- ĐẤT DỊCH VỤ
- ĐẤT BÃI ĐỖ XE ĐÔ THỊ
- ĐẤT HẠ TẦNG KỸ THUẬT KHÁC
- ĐẤT SÔNG SUỐI, KÊNH RẠCH

SƠ ĐỒ KẾT QUẢ THỦY LỰC TRONG GIỜ DÙNG NƯỚC LỚN NHẤT

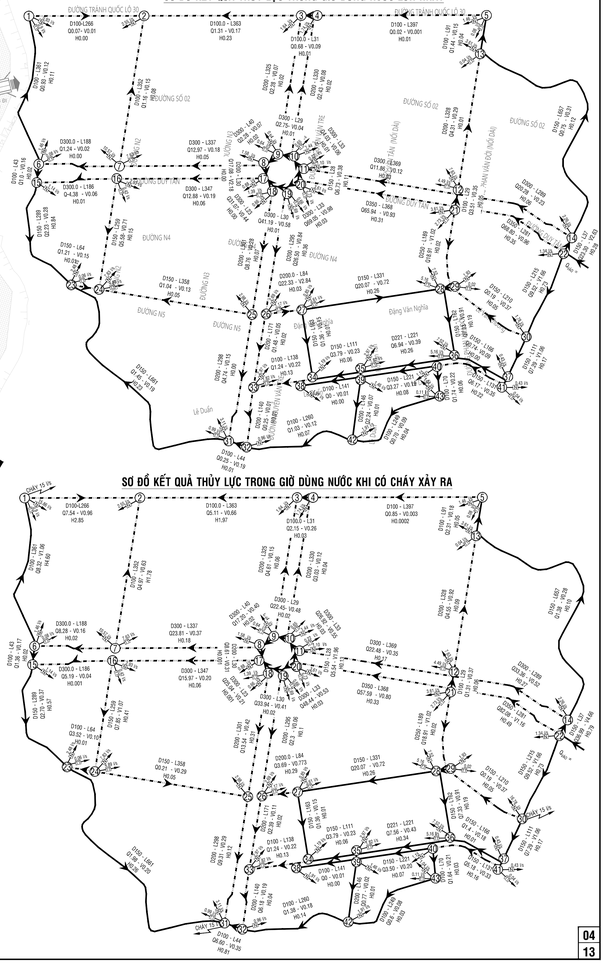

SƠ ĐỒ KẾT QUẢ THỦY LỰC TRONG GIỜ DÙNG NƯỚC KHI CÓ CHÁY XẢY RA