
ĐỒ ÁN TỐT NGHIỆP KỸ SƯ CƠ SỞ HẠ TẦNG ĐÔ THỊ KHÓA KD20

XÃ MỸ TRÀ - THÀNH PHỐ CAO LÃNH - TỈNH ĐỒNG THÁP


QUY HOẠCH HỆ THỐNG HẠ TẦNG KỸ THUẬT TỶ LỆ 1/2000 KHU DÂN CƯ RẠCH CHANH


BẢN ĐỒ QUY HOẠCH HỆ THỐNG THOÁT NƯỚC THẢI

SƠ ĐỒ VỊ TRÍ KHU ĐẤT QUY HOẠCH

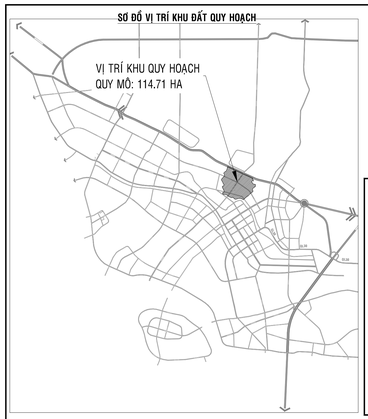

TRẮC DỌC TUYẾN CỐNG THOÁT NƯỚC THẢI ĐIỂN HÌNH TỪ HỐ GA 2.31 ĐẾN HỐ GA 2.32

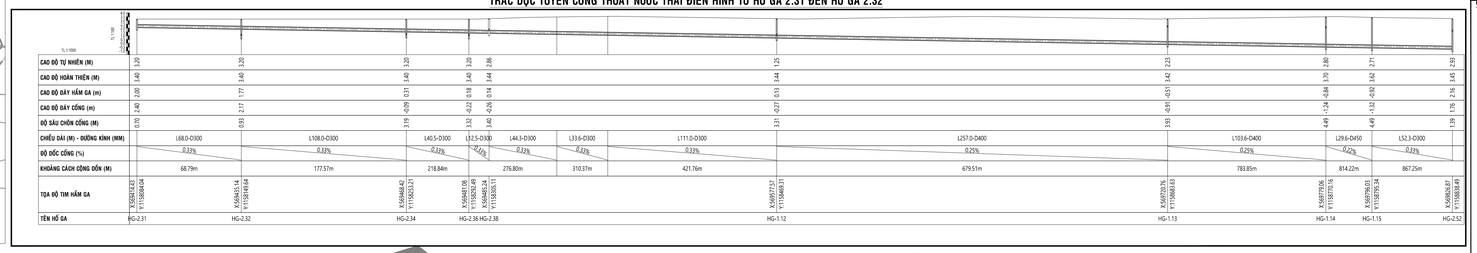

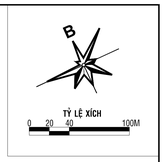

KÍ HIỆU


- HG1.3 / 1.55 / 3.45 — TÊN HỐ GA; CAO ĐỘ ĐÁY CỐNG (M); CAO ĐỘ XÂY DỰNG (M)
- 3.20 / 2.00 — CAO ĐỘ THIẾT KẾ (M); CAO ĐỘ TỰ NHIÊN (M)
- CỐNG THOÁT NƯỚC THẢI ÁP LỰC
- CỐNG THOÁT NƯỚC THẢI QUY HOẠCH
- MŨI TÊN CHỈ HƯỚNG LƯU VỰC
- L155-D1000-I0,18% — CHIỀU DÀI(M)- ĐƯỜNG KÍNH(MM)- ĐỘ DỐC(%); HƯỚNG DỐC CỐNG
- HỐ GA
- CỬA XẢ
- 1-1 — KÍ HIỆU MẶT CẮT
- TRẠM XỬ LÍ NƯỚC THẢI
- TRẠM BƠM TĂNG ÁP

BẢNG TỔNG HỢP KHỐI LƯỢNG THOÁT NƯỚC THẢI


STT	HẠNG MỤC	ĐƠN VỊ	KHỐI LƯỢNG
I	CỐNG TRÒN HDPE	M	12622
1.1	CỐNG D300	M	11110
1.2	CỐNG D350	M	1109
1.3	CỐNG D400	M	363
1.4	CỐNG D450	M	40
II	CỬA XẢ		1
III	BƠM TĂNG ÁP	BỘ	1
III	HỐ GA	HỐ	87


MẶT CẮT GIAO THÔNG ĐIỂN HÌNH



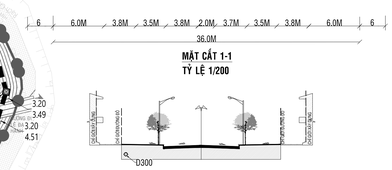


MẶT CẮT 1-1
TỶ LỆ 1/200

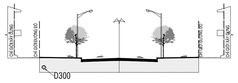

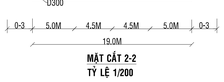

MẶT CẮT 2-2
TỶ LỆ 1/200

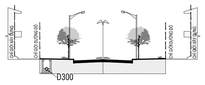



MẶT CẮT 3-3
TỶ LỆ 1/200

THUYẾT MINH SƠ BỘ

I. CƠ SỞ THIẾT KẾ:


- QCVN 07:2023/BXD QUY CHUẨN KỸ THUẬT QUỐC GIA VỀ QUY HOẠCH XÂY DỰNG.
- QCVN 01:2021/BXD QUY CHUẨN KỸ THUẬT QUỐC GIA CÁC CÔNG TRÌNH HẠ TẦNG KỸ THUẬT - CÔNG TRÌNH THOÁT NƯỚC.
- TCVN 7957:2023 THOÁT NƯỚC - MẠNG LƯỚI VÀ CÁC CÔNG TRÌNH BÊN NGOÀI - TIÊU CHUẨN THIẾT KẾ.

II. QUY MÔ VÀ SỐ LIỆU THOÁT NƯỚC:

- KHU VỰC QUY HOẠCH THUỘC KHU DÂN CƯ RẠCH CHANH, XÃ MỸ TRÀ, THÀNH PHỐ CAO LÃNH, TỈNH ĐỒNG THÁP VỚI DIỆN TÍCH KHOẢNG 114,71HA.
- THEO MÔ HÌNH TÍNH TOÁN LƯU LƯỢNG THOÁT NƯỚC, TỔNG LƯU LƯỢNG NƯỚC THẢI THU GOM LÀ 100% LƯU LƯỢNG NƯỚC SINH HOẠT.
- TỔNG LƯU LƯỢNG NƯỚC THẢI TOÀN KHU QUY HOẠCH: 3155 M³/NGÀY.ĐÊM.

III. GIẢI PHÁP THOÁT NƯỚC:

- NƯỚC THẢI SINH HOẠT TỪ CÁC CÔNG TRÌNH TRƯỚC KHI ĐỔ RA RẠCH GỒM CỤM CHUNG PHẢI ĐƯỢC XỬ LÝ CỤC BỘ, CÁC KHU VỰC SINH HOẠT PHẢI CÓ BỂ TỰ HOẠI.
- NƯỚC THẢI Y TẾ VÀ BỆNH ĐƯỢC PHẢI ĐƯỢC XỬ LÝ RIÊNG TRƯỚC KHI ĐƯA RA MẠNG LƯỚI.
- NƯỚC THẢI SAU XỬ LÝ ĐẠT CỘT A CỦA QCVN 14:2025/BTNMT SẼ ĐƯỢC XẢ RA RẠCH CHANH - NGUỒN TIẾP NHẬN PHÍA BẮC XÃ MỸ TRÀ.
- NƯỚC THẢI ĐƯỢC THU GOM TỪ CÁC TUYẾN CỐNG NHÁNH ĐỔ VỀ TUYẾN CHÍNH, BẮT ĐẦU TỪ HỐ GA 1.2 DẪN ĐẾN HỐ GA 1.7A. SAU ĐÓ SỬ DỤNG BƠM CHUYỂN BẬC ĐƯA NƯỚC THẢI ĐẾN HỐ GA 1.8, SAU ĐÓ TỰ CHẢY THEO DỐC CỐNG VÀ DẪN VỀ TRẠM XỬ LÍ PHÍA ĐÔNG BẮC. KHU QUY HOẠCH, CÓ CÔNG SUẤT HOẠT ĐỘNG DỰ KIẾN LÀ 3600 M³/NGÀY.ĐÊM.
- BỐ TRÍ CỐNG THOÁT NƯỚC THẢI DƯỚI VỈA HÈ VỚI ĐỘ SÂU CHÔN CỐNG TỪ 0.7-4.49M. VẬT LIỆU ỐNG CỐNG BẰNG ỐNG NHỰA CỨNG HDPE - HỆ THỐNG CỐNG THOÁT NƯỚC THẢI SỬ DỤNG ỐNG HDPE HOẶC BTCT ĐẶT TRONG MƯƠNG CỨNG CÓ KÈ BẢO VỆ 2 BÊN, TẠO ĐỘ BỀN CHẮC, KẾT HỢP CÁC HỐ GA THOÁT NƯỚC, HỐ GA KIỂM TRA THEO ĐỊNH KỲ, ĐẢM BẢO THUẬN TIỆN VỀ SINH MẠNG LƯỚI, TRÁNH TẮC NGHẼN.
- TRẠM TRUNG CHUYỂN CỤC BỘ ĐƯỢC BỐ TRÍ GẦN NHỮNG VÙNG THẤP, DÙNG BƠM CHÌM, KẾT HỢP VỚI 1 BƠM HÒA HOẠN, DÙNG ỐNG ĐẨY Ø75-Ø200.

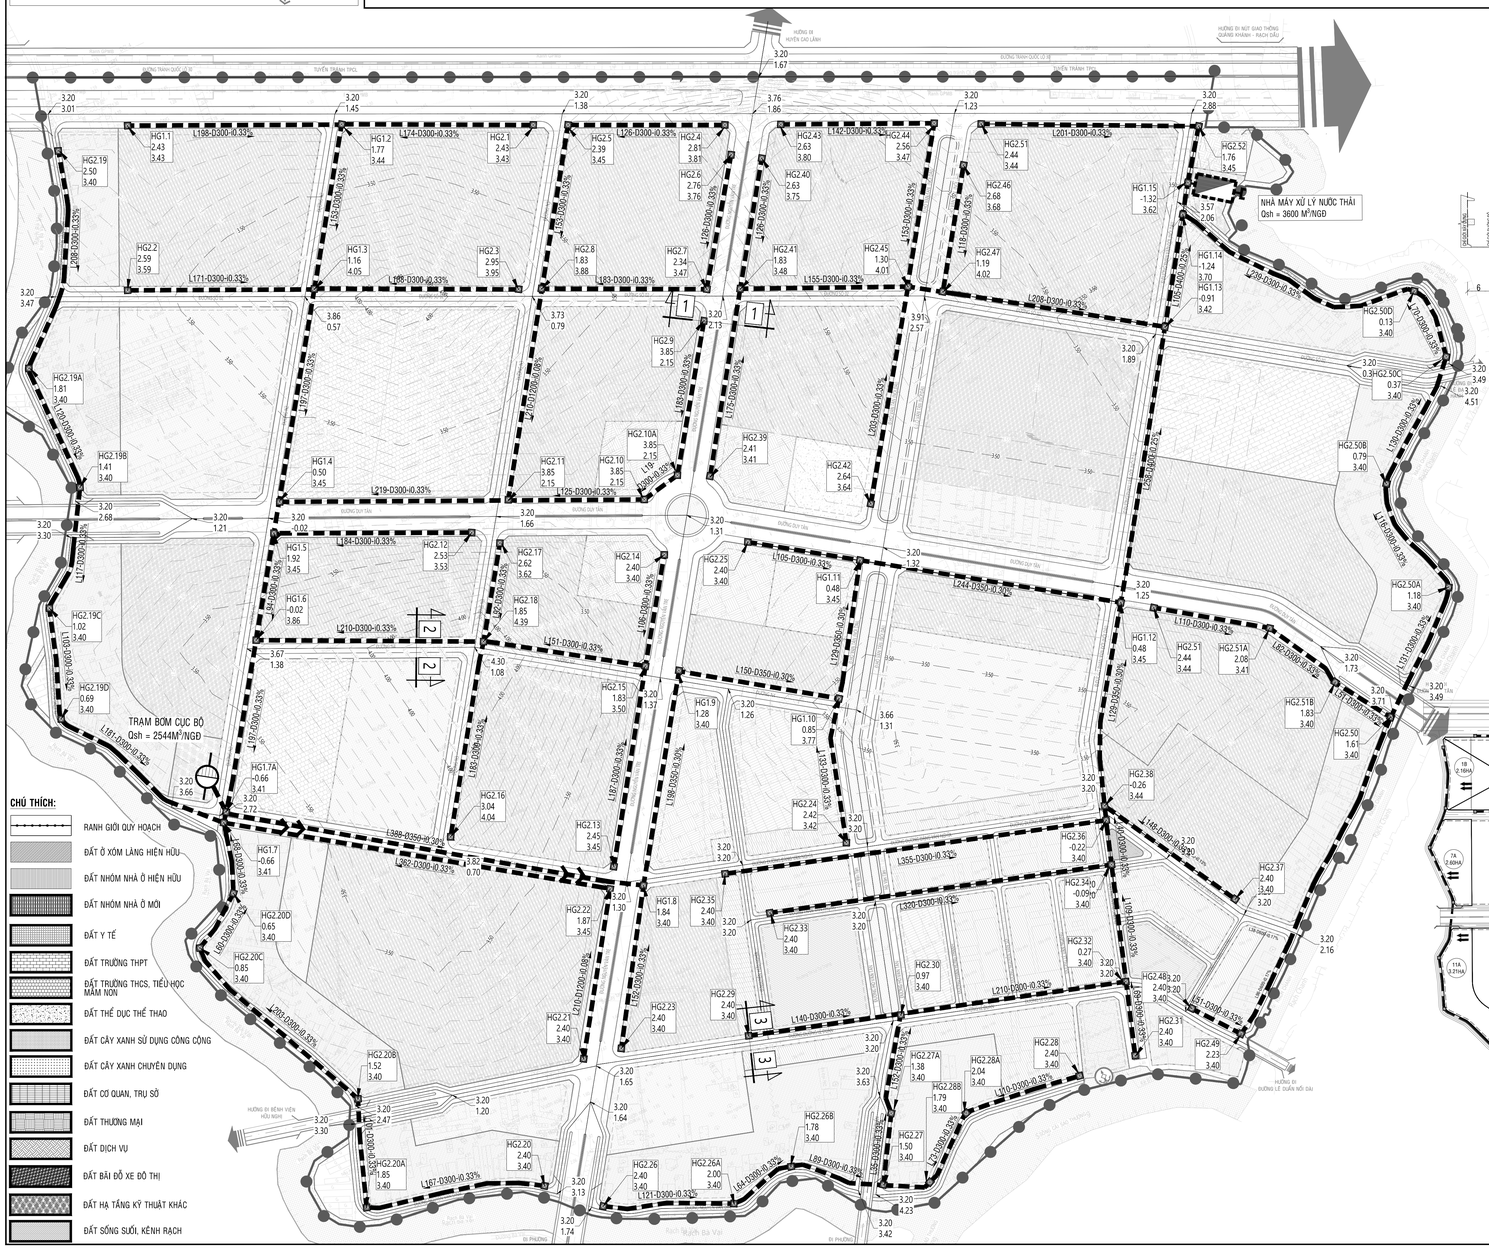

SƠ ĐỒ PHÂN CHIA LƯU VỰC THOÁT NƯỚC THẢI

