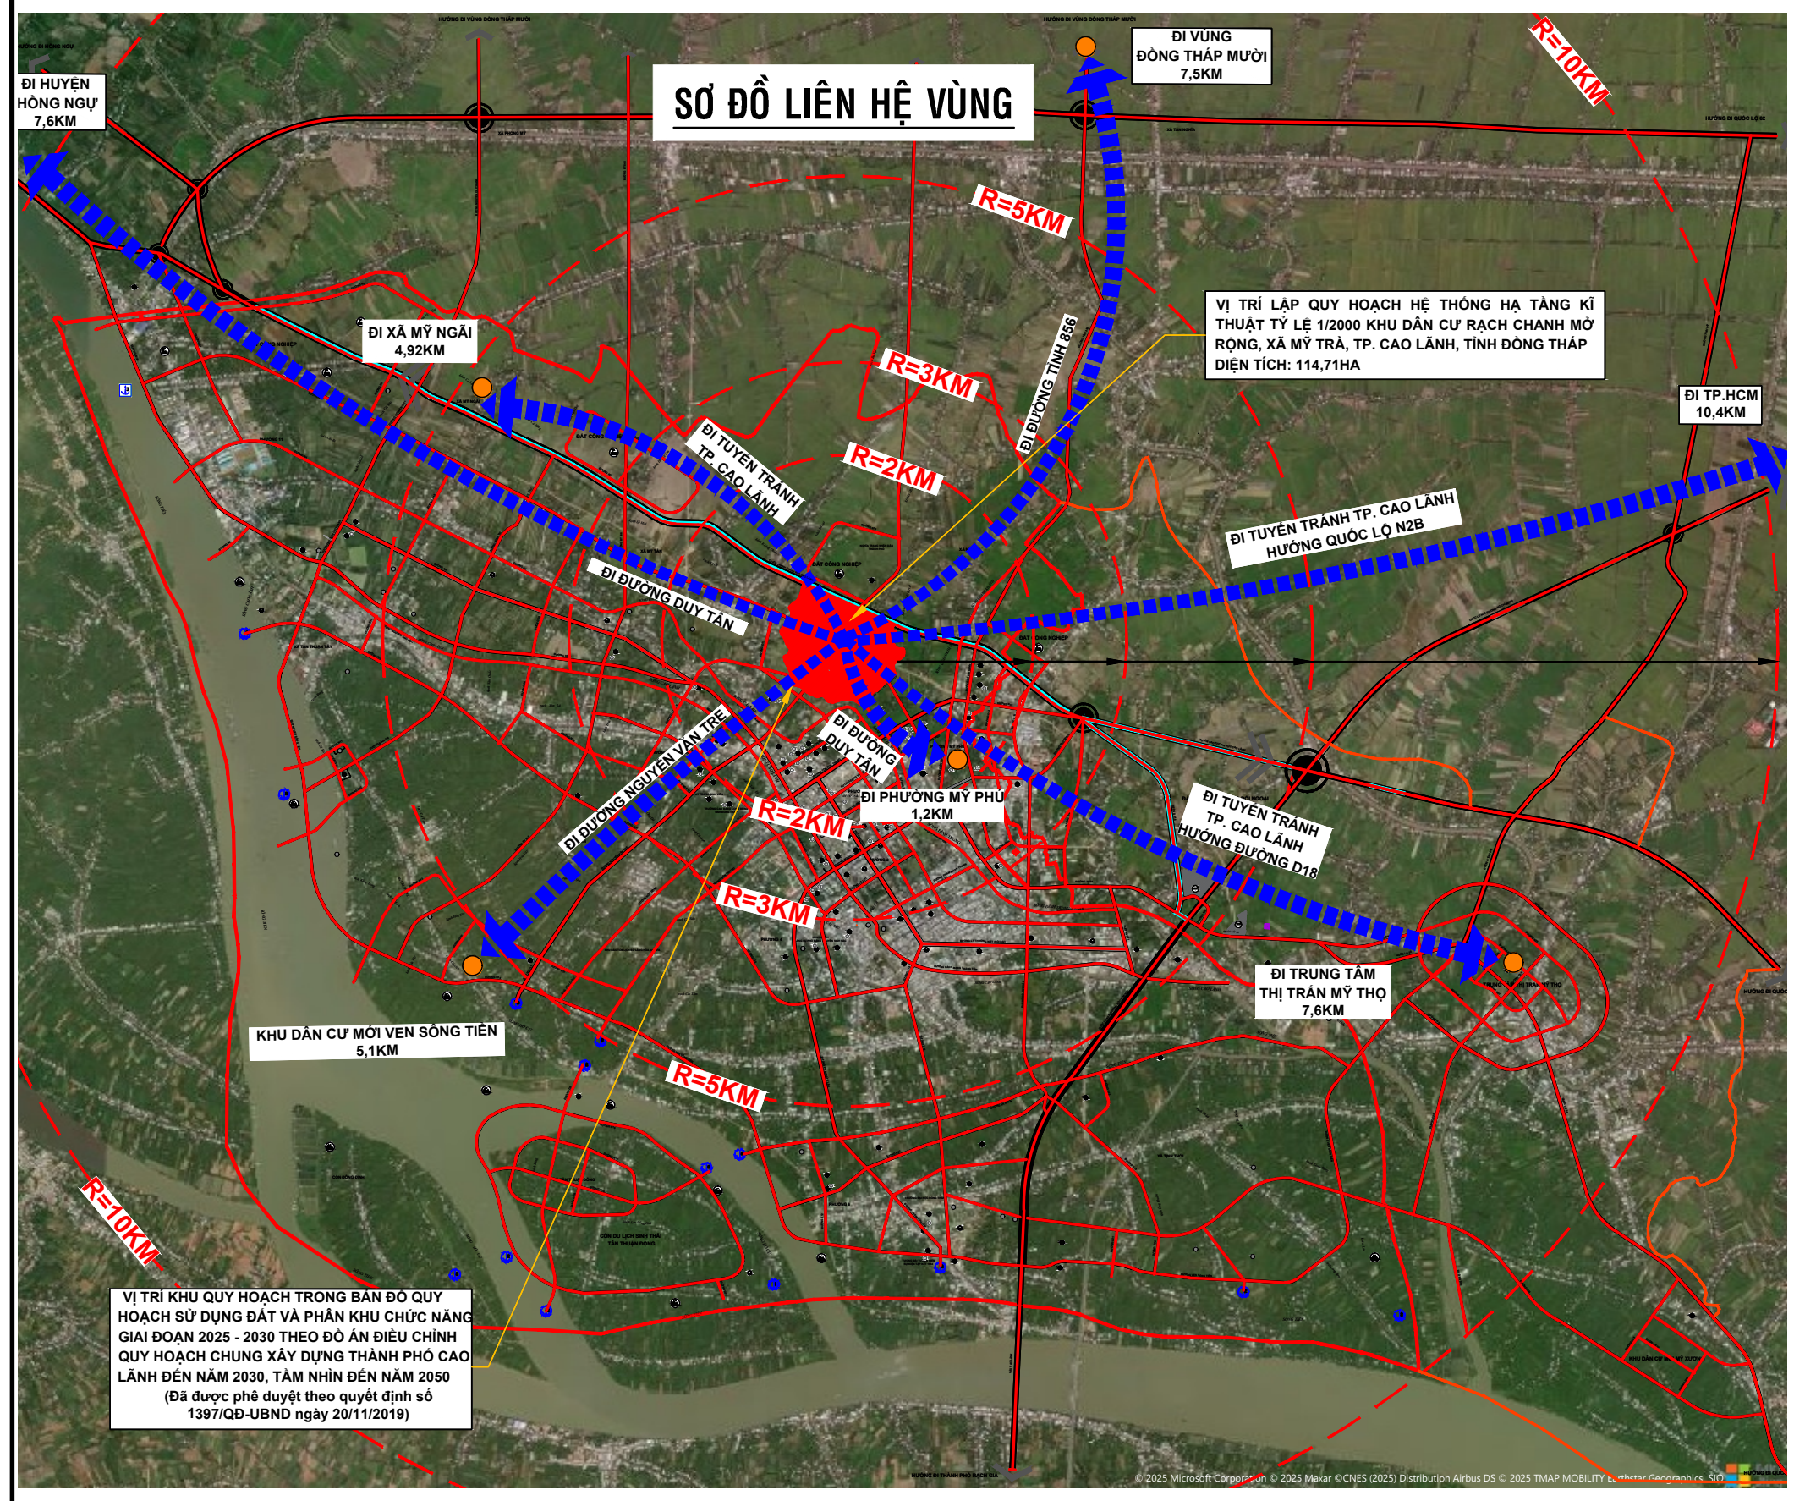
SƠ ĐỒ LIÊN HỆ VÙNG
ĐI HUYỆN HỒNG NGỰ 7,6KM
ĐI VÙNG ĐỒNG THÁP MƯỜI 7,5KM
R=10KM
R=5KM
R=3KM
R=2KM
VỊ TRÍ LẬP QUY HOẠCH HỆ THỐNG HẠ TẦNG KĨ THUẬT TỶ LỆ 1/2000 KHU DÂN CƯ RẠCH CHANH MỞ RỘNG, XÃ MỸ TRÀ, TP. CAO LÃNH, TỈNH ĐỒNG THÁP DIỆN TÍCH: 114,71HA
ĐI XÃ MỸ NGÃI 4,92KM
ĐI ĐƯỜNG TỈNH 856
ĐI TUYẾN TRÁNH TP. CAO LÃNH
ĐI TP.HCM 10,4KM
ĐI TUYẾN TRÁNH TP. CAO LÃNH HƯỚNG QUỐC LỘ N2B
ĐI ĐƯỜNG DUY TÂN
ĐI ĐƯỜNG NGUYỄN VĂN TRE
ĐI PHƯỜNG MỸ PHÚ 1,2KM
ĐI TUYẾN TRÁNH TP. CAO LÃNH HƯỚNG ĐƯỜNG D18
ĐI TRUNG TÂM THỊ TRẤN MỸ THỌ 7,6KM
KHU DÂN CƯ MỚI VEN SÔNG TIỀN 5,1KM
VỊ TRÍ KHU QUY HOẠCH TRONG BẢN ĐỒ QUY HOẠCH SỬ DỤNG ĐẤT VÀ PHÂN KHU CHỨC NĂNG GIAI ĐOẠN 2025 - 2030 THEO ĐỒ ÁN ĐIỀU CHỈNH QUY HOẠCH CHUNG XÂY DỰNG THÀNH PHỐ CAO LÃNH ĐẾN NĂM 2030, TẦM NHÌN ĐẾN NĂM 2050 (Đã được phê duyệt theo quyết định số 1397/QĐ-UBND ngày 20/11/2019)

ĐỒ ÁN TỐT NGHIỆP KỸ SƯ CƠ SỞ HẠ TẦNG ĐÔ THỊ KHÓA KD20

XÃ MỸ TRÀ - THÀNH PHỐ CAO LÃNH - TỈNH ĐỒNG THÁP

QUY HOẠCH HỆ THỐNG HẠ TẦNG KỸ THUẬT TỶ LỆ 1/2000 KHU DÂN CƯ RẠCH CHANH

BẢN ĐỒ ĐÁNH GIÁ HIỆN TRẠNG HẠ TẦNG KỸ THUẬT

TỶ LỆ XÍCH

0 20 40 100M

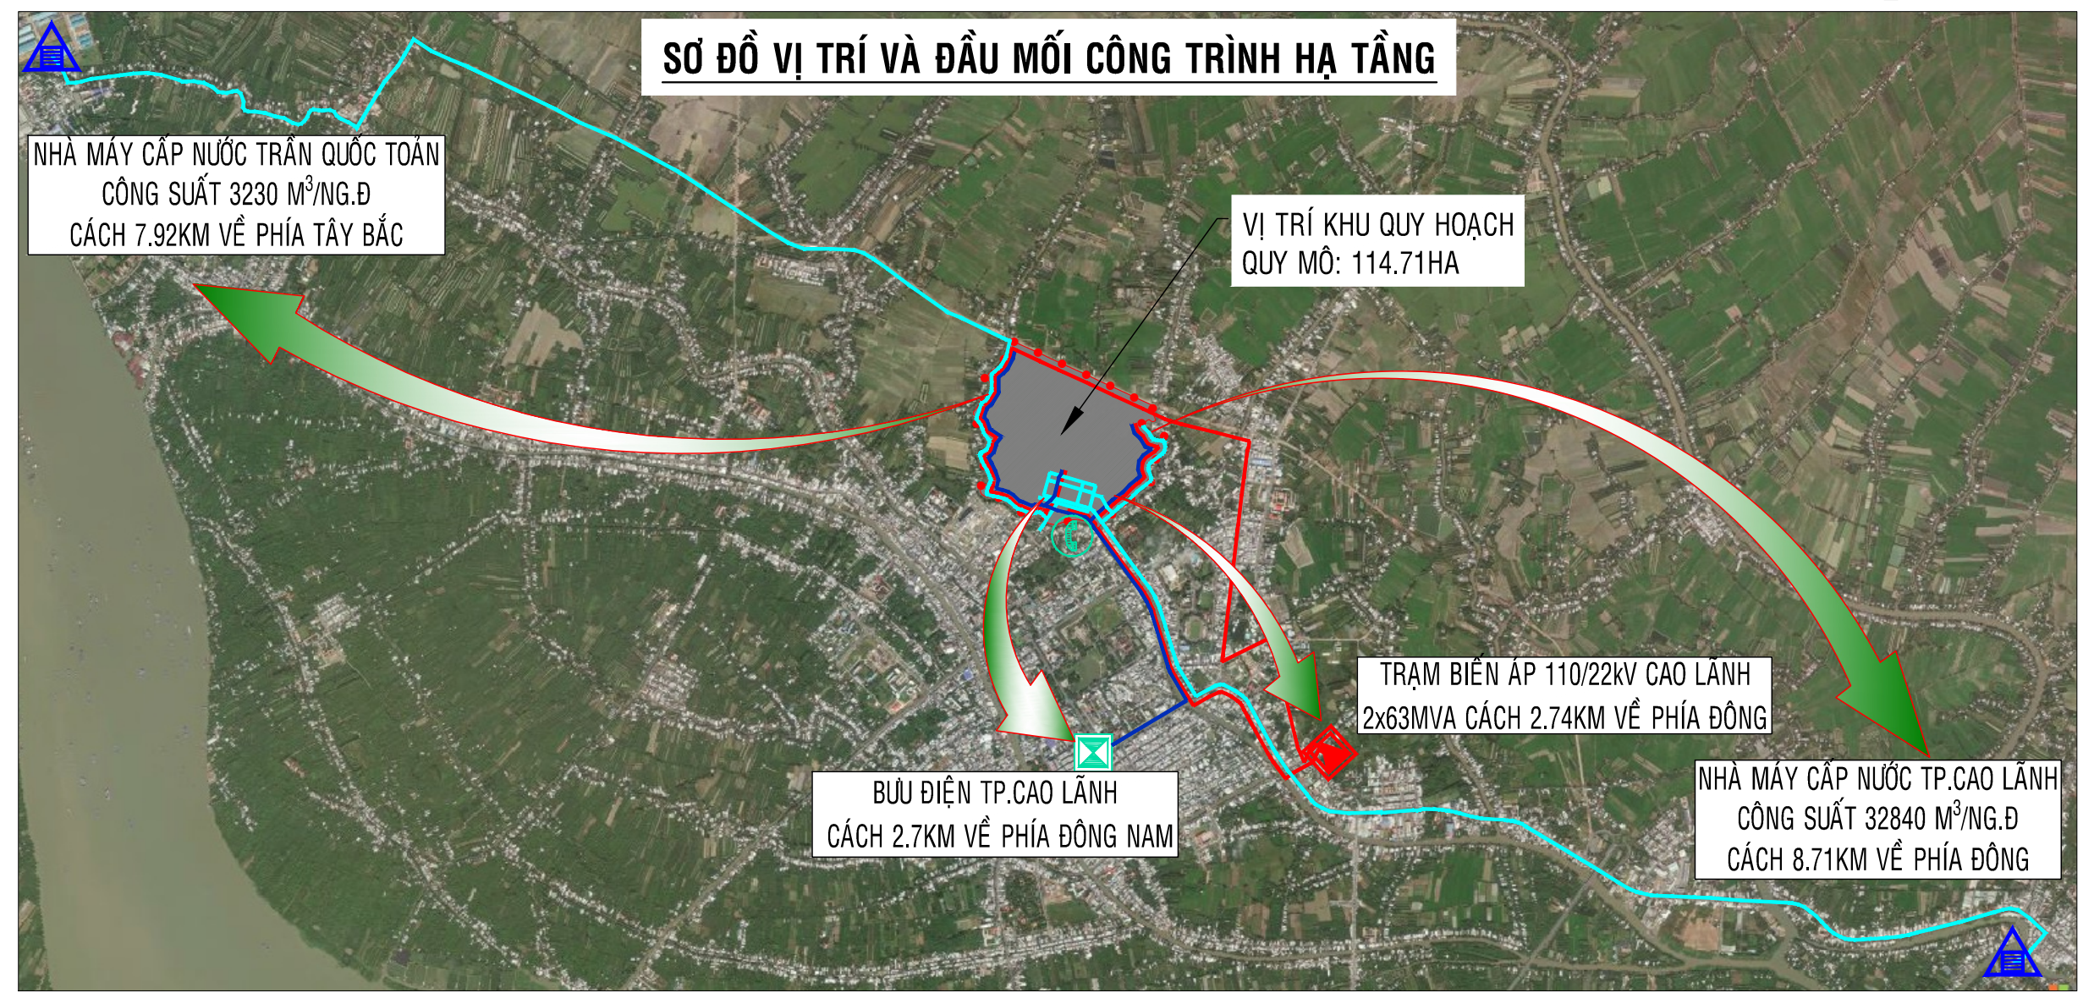
SƠ ĐỒ VỊ TRÍ VÀ ĐẦU MỐI CÔNG TRÌNH HẠ TẦNG
NHÀ MÁY CẤP NƯỚC TRẦN QUỐC TOẢN CÔNG SUẤT 3230 M³/NG.Đ CÁCH 7.92KM VỀ PHÍA TÂY BẮC
VỊ TRÍ KHU QUY HOẠCH QUY MÔ: 114.71HA
TRẠM BIẾN ÁP 110/22kV CAO LÃNH 2x63MVA CÁCH 2.74KM VỀ PHÍA ĐÔNG
BƯU ĐIỆN TP.CAO LÃNH CÁCH 2.7KM VỀ PHÍA ĐÔNG NAM
NHÀ MÁY CẤP NƯỚC TP.CAO LÃNH CÔNG SUẤT 32840 M³/NG.Đ CÁCH 8.71KM VỀ PHÍA ĐÔNG

CHÚ THÍCH

▲	TRẠM BIẾN ÁP 110kV HIỆN TRẠNG	⧖	TỔNG ĐÀI BƯU ĐIỆN HIỆN TRẠNG
△	NHÀ MÁY CẤP NƯỚC HIỆN TRẠNG	☎	TRẠM ĐIỆN THOẠI HIỆN TRẠNG

BẢNG PHÂN TÍCH CAO ĐỘ HIỆN TRẠNG

STT	TỪ CAO ĐỘ	ĐẾN CAO ĐỘ	MÀU	DIỆN TÍCH (HA)
1	-1.50	0.00	🟧	1.80
2	0.00	1.00	🟧	14.70
3	1.00	2.00	🟨	61.70
4	2.00	5.00	🟩	40.70
5	5.00	8.00	🟩	0.10

BÌNH ĐỒ CAO ĐỘ NỀN HIỆN TRẠNG THEO MÀU

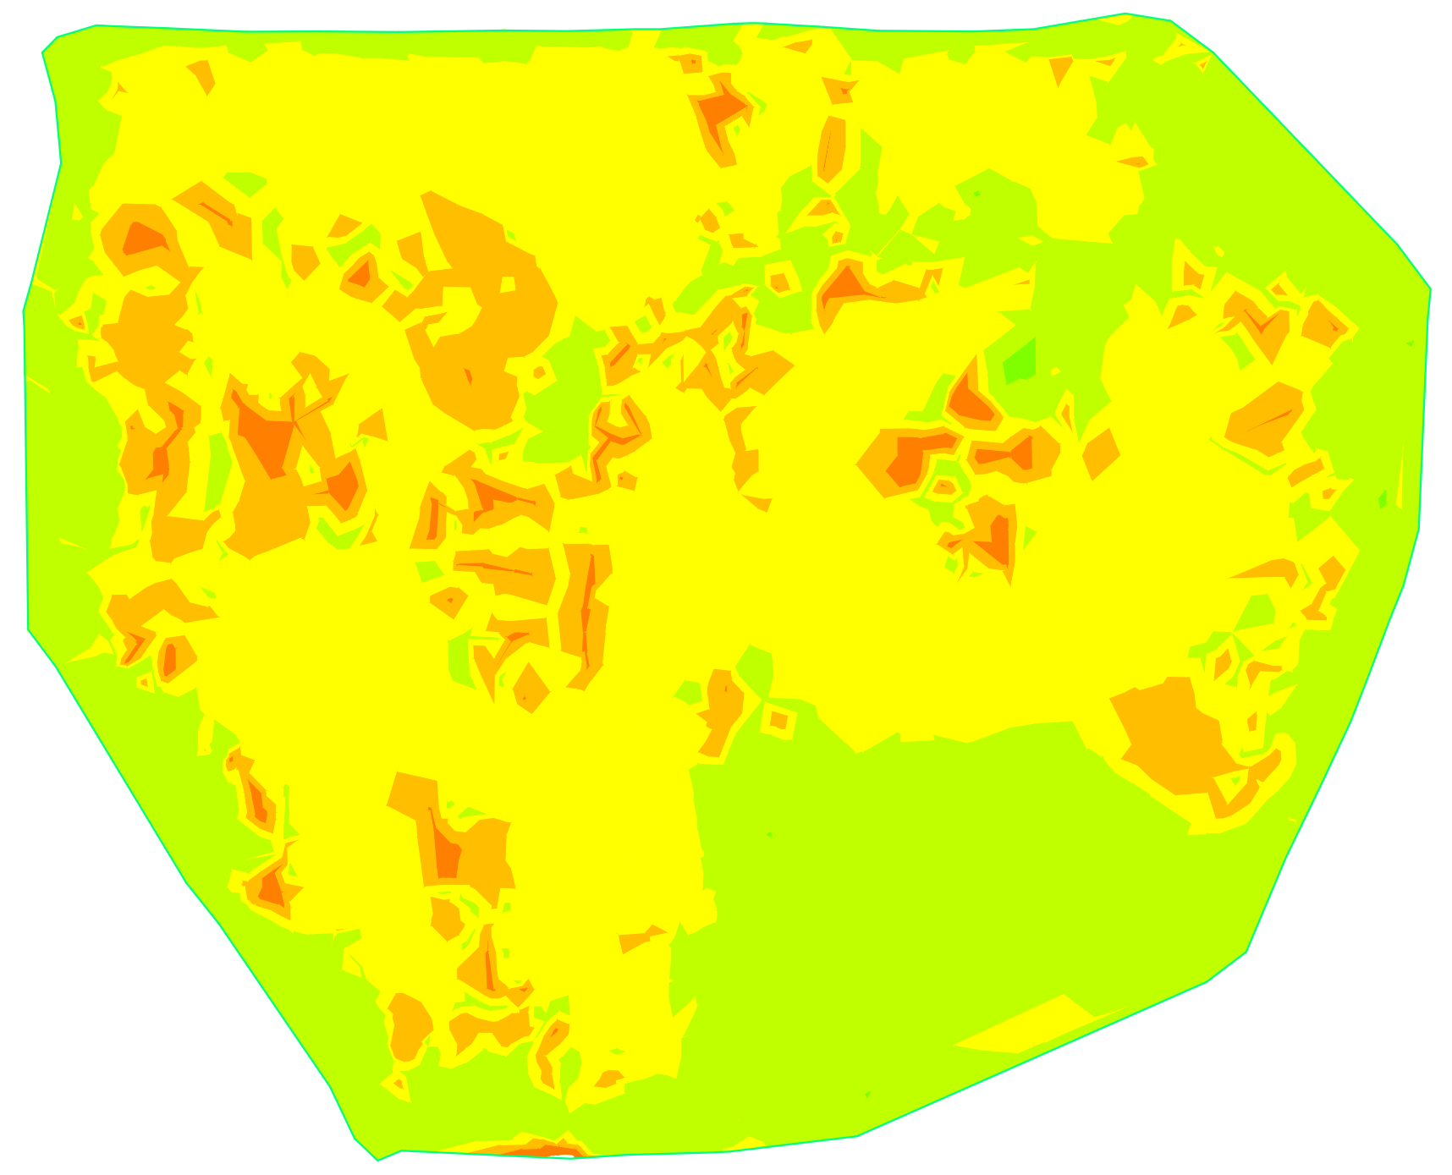

KÍ HIỆU

⚓	BẾN THUYỀN
▬	GIAO THÔNG HIỆN TRẠNG NHỰA, BÊ TÔNG XI MĂNG
D800	ĐƯỜNG KÍNH CỐNG THOÁT NƯỚC MƯA
━	CỐNG THOÁT NƯỚC MƯA HIỆN HỮU
Ø200	ĐƯỜNG KÍNH ỐNG
━	ỐNG CẤP NƯỚC HIỆN HỮU
━ 22KV ━	ĐƯỜNG DÂY 22KV ĐI NỔI HIỆN HỮU
1 — 1	KÍ HIỆU MẶT CẮT

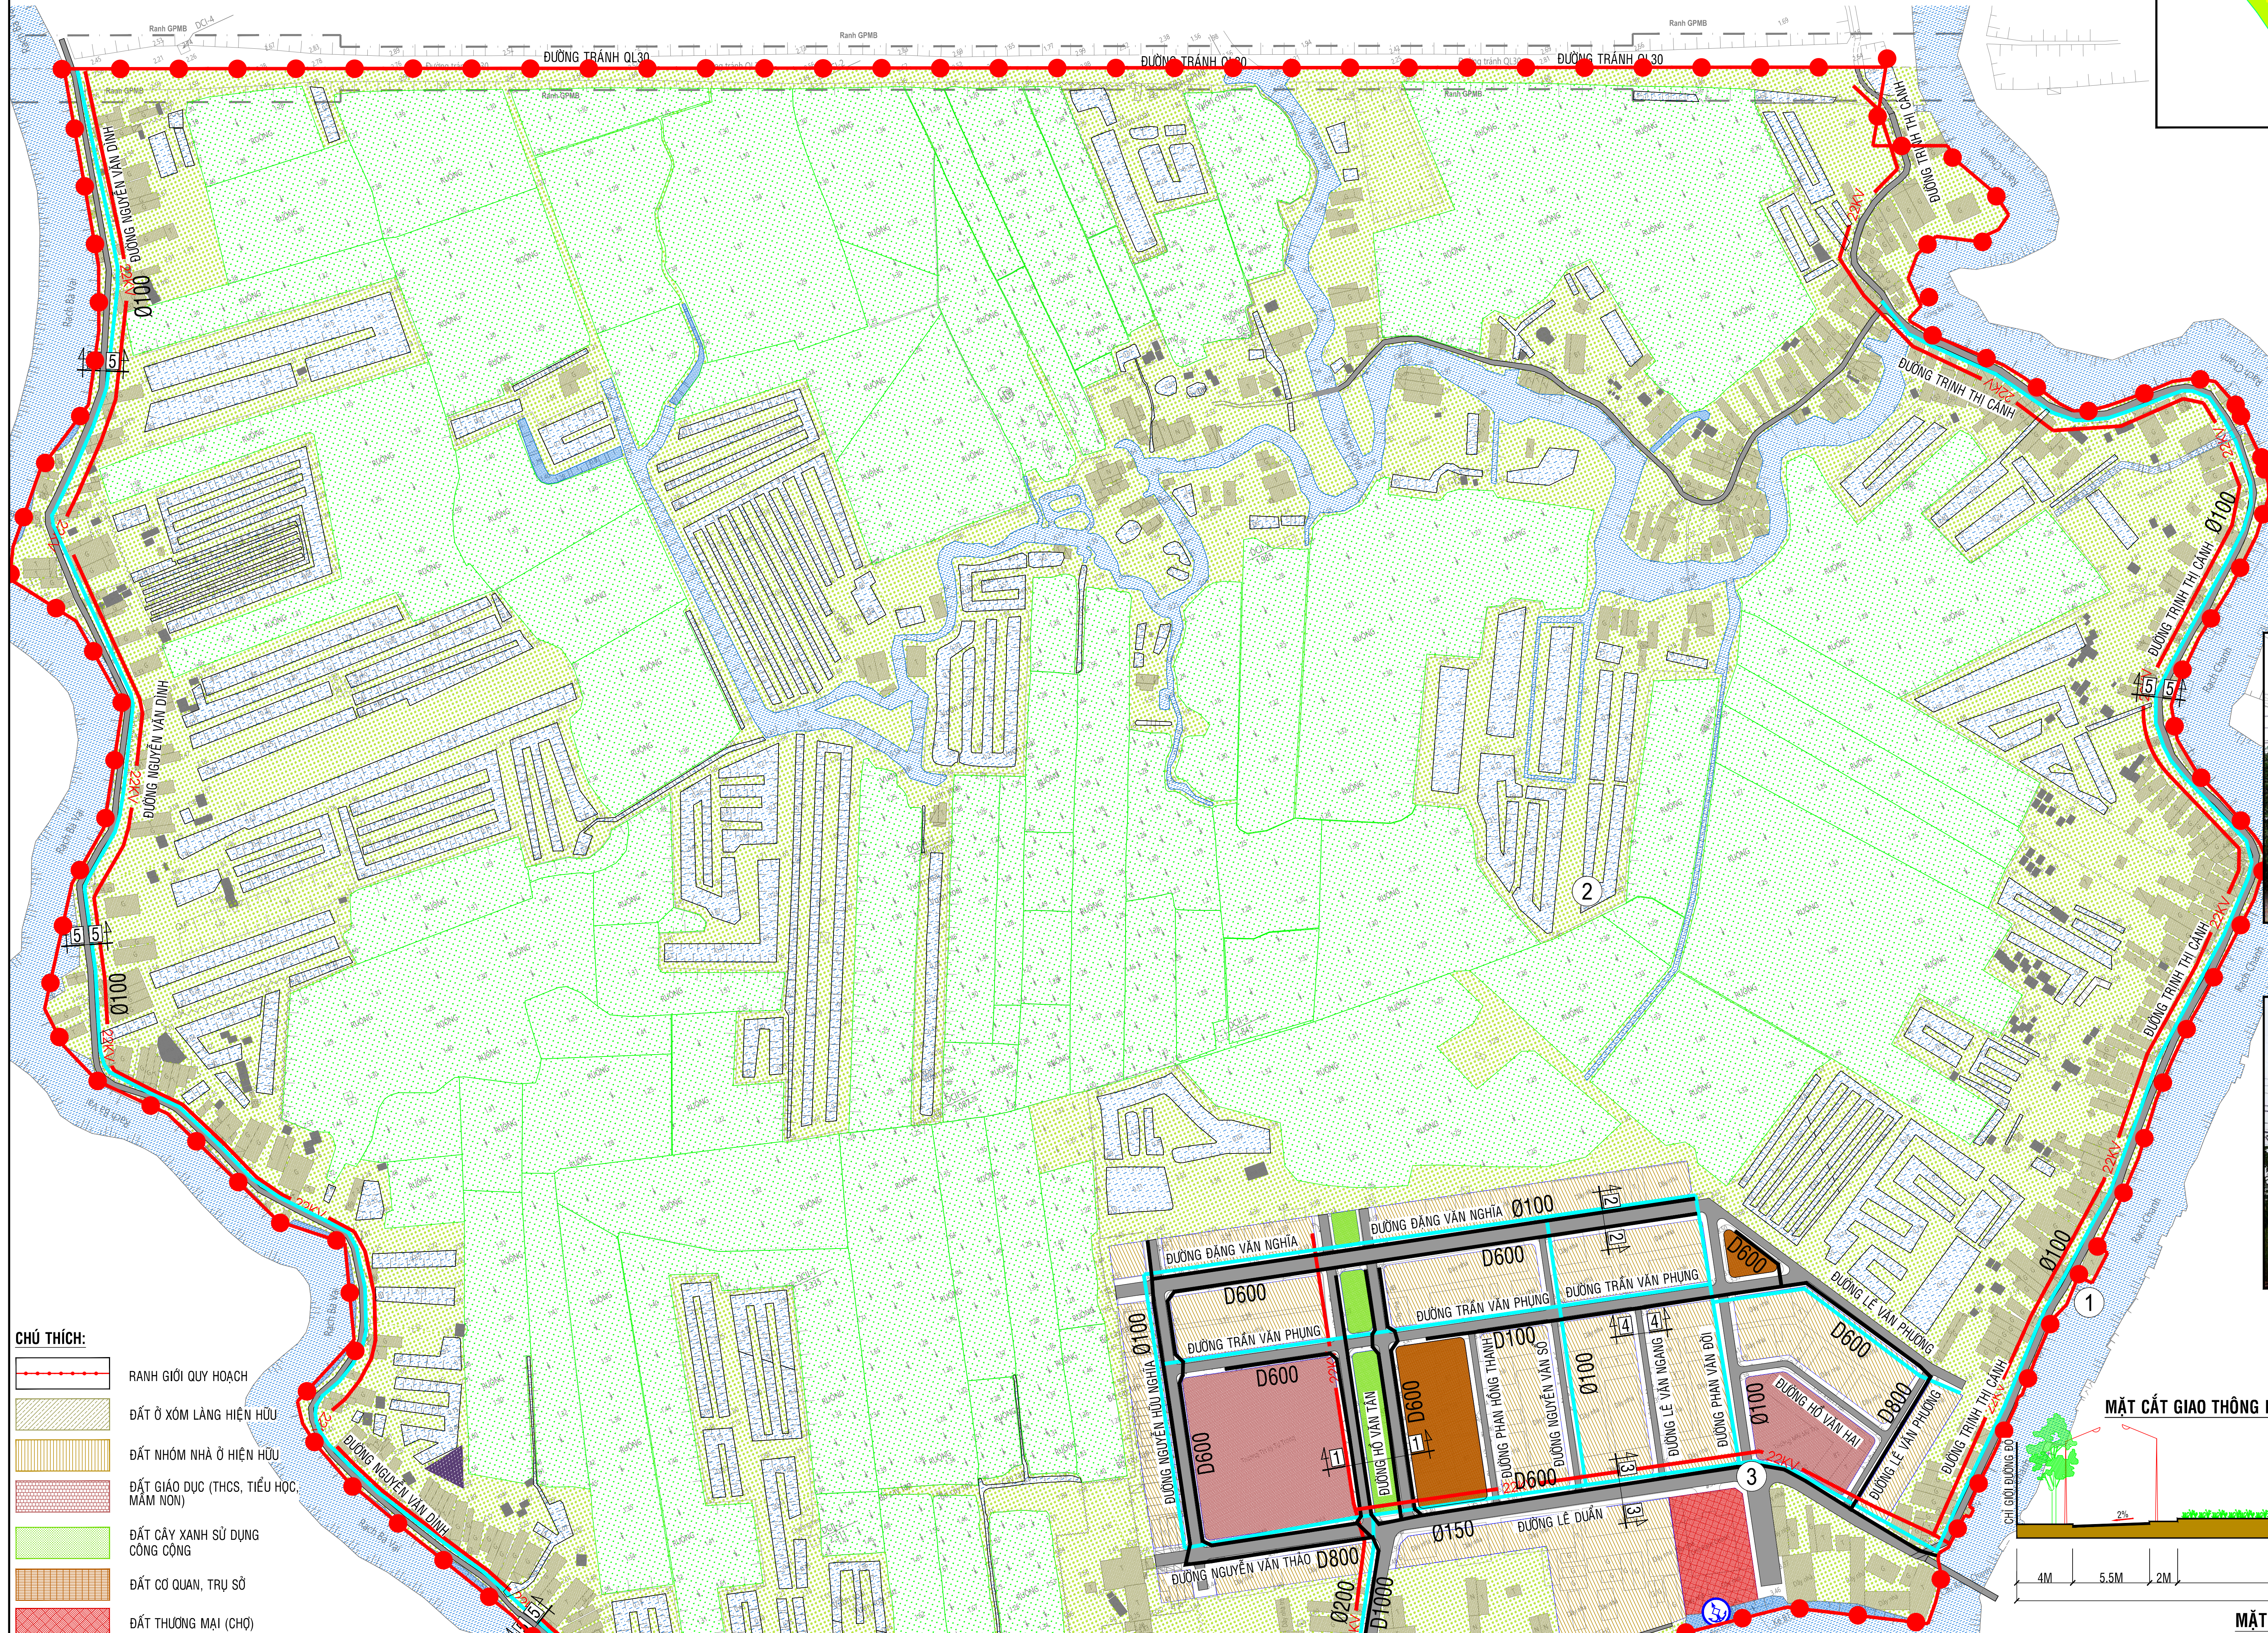

CHÚ THÍCH:

─●─●─	RANH GIỚI QUY HOẠCH
▨	ĐẤT Ở XÓM LÀNG HIỆN HỮU
▥	ĐẤT NHÓM NHÀ Ở HIỆN HỮU
▦	ĐẤT GIÁO DỤC (THCS, TIỂU HỌC, MẦM NON)
🟩	ĐẤT CÂY XANH SỬ DỤNG CÔNG CỘNG
▦	ĐẤT CƠ QUAN, TRỤ SỞ
🟥	ĐẤT THƯƠNG MẠI (CHỢ)
▒	ĐẤT NGHĨA TRANG, NGHĨA ĐỊA
▒	ĐẤT SẢN XUẤT NÔNG NGHIỆP (TRỒNG LÚA)
▨	ĐẤT SẢN XUẤT NÔNG NGHIỆP (TRỒNG TRỌT KHÁC)
▤	HỒ, AO, ĐẦM
▤	SÔNG, SUỐI, KÊNH, RẠCH

BẢNG CÂN BẰNG ĐẤT ĐAI

STT	CHỨC NĂNG	DIỆN TÍCH (M^2)	TỶ LỆ (%)
I	**ĐẤT Ở HIỆN TRẠNG**	107520.47	9.37
1.1	ĐẤT Ở LÀNG XÓM	60539.35	
1.2	ĐẤT NHÓM NHÀ Ở	46981.12	
II	**ĐẤT GIÁO DỤC**		1.07
2.1	TRƯỜNG TIỂU HỌC LÝ TỰ TRỌNG	8909.93	
2.2	TRƯỜNG MẦM NON MỸ TRÀ	3338.59	
III	**ĐẤT CÂY XANH CÔNG CỘNG**	2313.21	0.20
IV	**ĐẤT CƠ QUAN TRỤ SỞ**	4577.50	0.40
4.1	ỦY BAN NHÂN DÂN XÃ MỸ TRÀ	4371.27	
4.2	BAN CHỈ HUY QUÂN SỰ	205.73	
V	**ĐẤT THƯƠNG MẠI**	3060.34	0.27
5.1	CHỢ RẠCH CHANH	3060.34	
VI	**ĐẤT GIAO THÔNG**	28996.85	2.53
VII	**ĐẤT NGHĨA TRANG, NGHĨA ĐỊA**	4775.29	0.42
VIII	**ĐẤT SẢN XUẤT NÔNG NGHIỆP**	838893.67	73.13
8.1	ĐẤT TRỒNG LÚA	504298.20	
8.2	ĐẤT TRỒNG TRỌT KHÁC	334595.47	
IX	**HỒ, AO, ĐẦM**	101944.51	8.89
X	**SÔNG, SUỐI, KÊNH, RẠCH**	42804.18	3.73
TỔNG		1147134.04	100.00

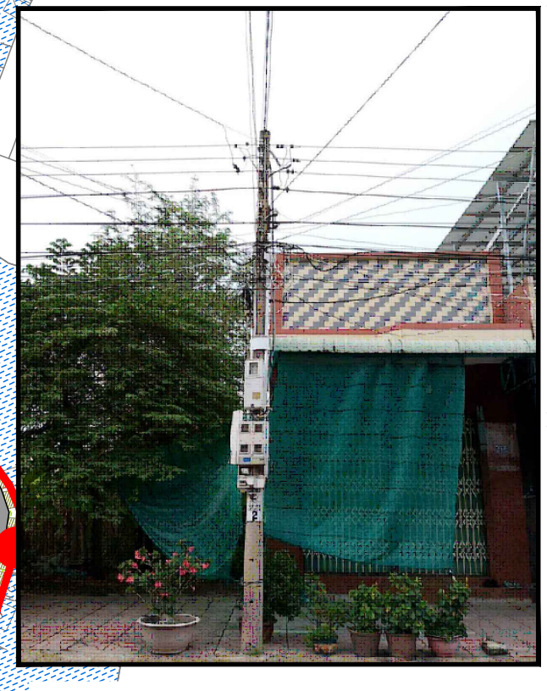

TUYẾN ĐIỆN ĐI TRÊN KHÔNG ĐƯỜNG ĐẶNG VĂN NGHĨA

HIỆN TRẠNG RẠCH CHANH

HIỆN TRẠNG MƯƠNG TƯỚI

CỘT ĐÈN CHIẾU SÁNG ĐƯỜNG ĐẶNG VĂN NGHĨA

CỐNG THOÁT NƯỚC THẢI HỘ DÂN

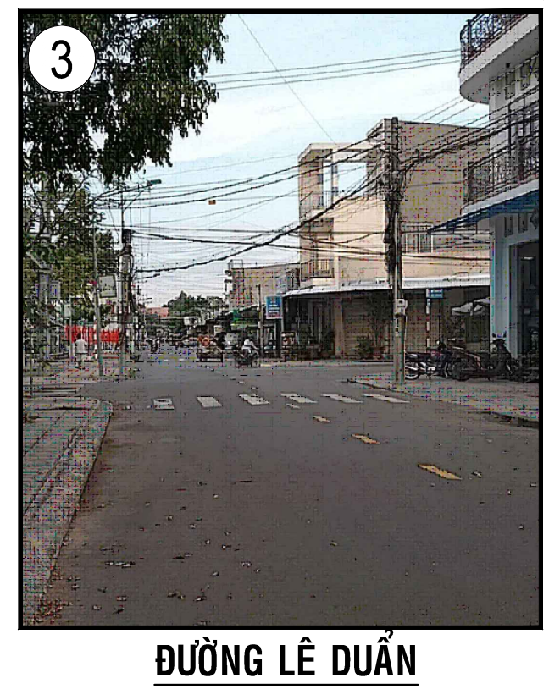

ĐƯỜNG LÊ DUẨN

THUYẾT MINH SƠ BỘ

I. TỔNG QUAN VỀ KHU ĐẤT QUY HOẠCH:

1.1. VỊ TRÍ VÀ PHẠM VI GIỚI HẠN:

- KHU QUY HOẠCH THUỘC XÃ MỸ TRÀ, THÀNH PHỐ CAO LÃNH, TỈNH ĐỒNG THÁP. KHU VỰC NÀY NẰM TRONG ĐỊNH HƯỚNG MỞ RỘNG KHÔNG GIAN ĐÔ THỊ VỀ PHÍA ĐÔNG BẮC THÀNH PHỐ, PHÙ HỢP VỚI QUY HOẠCH CHUNG TP. CAO LÃNH TỶ LỆ 1/5000 ĐƯỢC PHÊ DUYỆT THEO QUYẾT ĐỊNH SỐ 1397/QĐ-UBND NGÀY 20/11/2019.
- RANH GIỚI QUY HOẠCH ĐƯỢC XÁC ĐỊNH NHƯ SAU:
  - PHÍA BẮC: GIÁP TUYẾN ĐƯỜNG TRÁNH THÀNH PHỐ CAO LÃNH.
  - PHÍA NAM: GIÁP SÔNG CÁI SAO THƯỢNG VÀ RẠCH BÀ VẠI.
  - PHÍA ĐÔNG: GIÁP RẠCH CHANH VÀ MỘT PHẦN KHU VỰC PHƯỜNG MỸ PHÚ.
  - PHÍA TÂY: GIÁP RẠCH BÀ VẠI.

1.2. QUY MÔ DIỆN TÍCH:

- KHU ĐẤT CÓ QUY MÔ 114.71HA, TỌA ĐỘ RANH QUY HOẠCH THỂ HIỆN TRÊN BẢN ĐỒ HIỆN TRẠNG.

II. ĐÁNH GIÁ HIỆN TRẠNG HẠ TẦNG KĨ THUẬT:

2.1. VỀ GIAO THÔNG:

A. GIAO THÔNG ĐỐI NGOẠI:

- KHU VỰC QUY HOẠCH HIỆN ĐÃ CÓ TUYẾN ĐƯỜNG DALE CHẠY DỌC BỜ KÊNH NHƯ ĐƯỜNG: NGUYỄN VĂN DÌNH, TRỊNH THỊ CÁNH, LÊ DUẨN CÓ QUY MÔ HIỆN TRẠNG BỀ RỘNG MẶT ĐƯỜNG NHỎ HẸP DỌC CÁC KÊNH RẠCH, SONG ĐÃ XUỐNG CẤP.
- KHU QUY HOẠCH NẰM TRONG ĐỀ ÁN QUỐC GIA XÂY DỰNG TUYẾN ĐƯỜNG TRÁNH TP CAO LÃNH CÙNG VỚI QUỐC LỘ 30 SONG HÀNH.
- KHU VỰC QUY HOẠCH CÓ CÁC TUYẾN SÔNG RẠCH BAO QUANH THUẬN LỢI PHÁT TRIỂN GIAO THÔNG ĐƯỜNG THỦY.

B. GIAO THÔNG ĐỐI NỘI:

- KHU QUY HOẠCH CÓ KHU DÂN CƯ RẠCH CHANH HIỆN HỮU ĐÃ ĐƯỢC QUY HOẠCH ĐƯỜNG GIAO THÔNG TRẢI NHỰA HOÀN CHỈNH. QUY MÔ LỘ GIỚI HIỆN TRẠNG 9.5M-38M.

2.2. VỀ SAN NỀN THOÁT NƯỚC MƯA:

- HỆ THỐNG THOÁT NƯỚC MƯA ĐÃ ĐƯỢC XÂY DỰNG TRÊN MỘT SỐ TUYẾN ĐƯỜNG NHƯ ĐƯỜNG TÔN ĐỨC THẮNG, TRẦN VĂN PHỤNG, ĐƯỜNG LÊ DUẪN,...ĐƯỜNG KÍNH Ø600-Ø1000
- PHẦN LỚN KHU VỰC LÀ ĐẤT NÔNG NGHIỆP NÊN CHƯA CÓ HỆ THỐNG THOÁT NƯỚC MƯA. CÁC KHU VỰC CHƯA XÂY DỰNG, NƯỚC MƯA ĐƯỢC THOÁT TỰ NHIÊN THEO ĐỊA HÌNH RA CÁC AO HỒ, RẠCH, SUỐI HIỆN HỮU.

2.3. VỀ CẤP NƯỚC:

- KHU VỰC QUY HOẠCH TRÊN CÁC TRỤC ĐƯỜNG CHÍNH TẬP TRUNG DÂN CƯ SINH SỐNG ĐÃ CÓ CÁC TUYẾN ỐNG CẤP NƯỚC Ø100 VỚI TỔNG CHIỀU DÀI KHOẢNG 4053M CẤP NƯỚC SINH HOẠT VÀ CHỮA CHÁY CHO DÂN CƯ KHU VỰC QUY HOẠCH. NGUỒN NƯỚC CHÍNH CẤP CHO KHU VỰC TỪ NHÀ MÁY NƯỚC CAO LÃNH.
- TỶ LỆ HỘ DÂN ĐƯỢC CẤP NƯỚC SINH HOẠT 97,04%.

2.4. VỀ THOÁT NƯỚC THẢI:

- THÀNH PHỐ CAO LÃNH HIỆN ĐÃ XÂY DỰNG HỆ THỐNG THOÁT NƯỚC THẢI RIÊNG KHÁ HOÀN CHỈNH, NHƯNG CHỈ TẬP TRUNG Ở KHU VỰC TRUNG TÂM THÀNH PHỐ. TRẠM XỬ LÝ NƯỚC THẢI CÓ CÔNG SUẤT 10.000 M^3/NGÀY ĐÊM. PHẦN CÒN LẠI NƯỚC THẢI SINH HOẠT THOÁT CHUNG VỚI HỆ THỐNG THOÁT NƯỚC MƯA HOẶC THOÁT TRỰC TIẾP RA CÁC SÔNG RẠCH GẦN NHẤT.
- HIỆN NAY TRONG KHU VỰC QUY HOẠCH CHƯA ĐƯỢC ĐẦU TƯ XÂY DỰNG HỆ THỐNG THOÁT NƯỚC THẢI SINH HOẠT. NƯỚC THẢI HẦU NHƯ KHÔNG ĐƯỢC XỬ LÝ HOẶC XỬ LÝ SƠ BỘ RỒI XẢ TRỰC TIẾP RA CỐNG RÃNH, SÔNG RẠCH NÊN GÂY Ô NHIỄM MÔI TRƯỜNG, NHẤT LÀ Ô NHIỄM CHO NGUỒN NƯỚC.

2.5. VỀ CẤP ĐIỆN:

- NGUỒN CẤP ĐIỆN CHO KHU QUY HOẠCH ĐƯỢC LẤY CHÍNH TỪ TRẠM 110/22KV CAO LÃNH, CÔNG SUẤT 2x63MVA THÔNG QUA CÁC TUYẾN 22KV TRÊN ĐƯỜNG LÊ DUẨN, PHÙNG KHẮC KHOAN, NGUYỄN VĂN DÌNH, ĐIỆN BIÊN PHỦ...DẪN TỚI.
- MẠNG LƯỚI ĐIỆN 0.4KV LẠI CHƯA HOÀN CHỈNH, CHỈ CÓ Ở KHU DÂN CƯ HIỆN HỮU.

2.6. VỀ THÔNG TIN LIÊN LẠC:

- KHU VỰC QUY HOẠCH CHƯA CÓ HỆ THỐNG CÁP QUANG THÔNG TIN LIÊN LẠC. KHU VỰC HIỆN HỮU CHỈ CÓ TUYẾN DÂY CÁP ĐIỆN THOẠI LÕI ĐỒNG ĐI CHUNG VỚI TUYẾN DÂY ĐIỆN TRÊN KHÔNG.

III. NHẬN XÉT ĐÁNH GIÁ HIỆN TRẠNG:

- NHÌN CHUNG, NGUỒN ĐIỆN CẤP CHO KHU VỰC QUY HOẠCH TỪ TRẠM 110/22KV CAO LÃNH -2X63MVA ĐỦ KHẢ NĂNG ĐÁP ỨNG NHU CẦU CẤP ĐIỆN KHU QUY HOẠCH.
- LƯỚI ĐIỆN: LƯỚI ĐIỆN TRUNG THẾ, HẠ THẾ TRÊN ĐỊA BÀN HUYỆN LÀ ĐA PHẦN LÀ ĐƯỜNG DÂY NỔI, TRẠM BIẾN THẾ LÀ LOẠI TRẠM NGOÀI TRỜI ĐÁP ỨNG YÊU CẦU VỀ KỸ THUẬT ĐIỆN, CÒN CÁC KHU VỰC THƯA DÂN CÁC TUYẾN TRUNG THẾ, HẠ THẾ KÉO DÀI DẪN TỚI TỔN HAO NHIỀU, TRONG THỜI GIAN TỚI CẦN CẢI TẠO, NÂNG CẤP, XÂY DỰNG MỚI CÁC TUYẾN TRUNG THẾ VÀ HẠ THẾ ĐỂ ĐÁP ỨNG NHU CẦU VỀ ĐIỆN.
- HIỆN ĐÃ CÓ 100% HỘ SỬ DỤNG ĐIỆN LƯỚI QUỐC GIA. TẠI CÁC TUYẾN GIAO THÔNG CƠ BẢN ĐÃ ĐƯỢC ĐẦU TƯ HỆ THỐNG CHIẾU SÁNG.
- KHU QUY HOẠCH ĐANG ĐƯỢC ĐẦU TƯ HỆ THỐNG CẤP ĐIỆN CŨNG NHƯ CÁC HẠ TẦNG ĐÔ THỊ KHÁC HƯỚNG TỚI NĂM 2030 THÀNH PHỐ CAO LÃNH ĐẠT TIÊU CHÍ CỦA ĐÔ THỊ LOẠI I.

MẶT CẮT GIAO THÔNG HIỆN TRẠNG ĐIỂN HÌNH

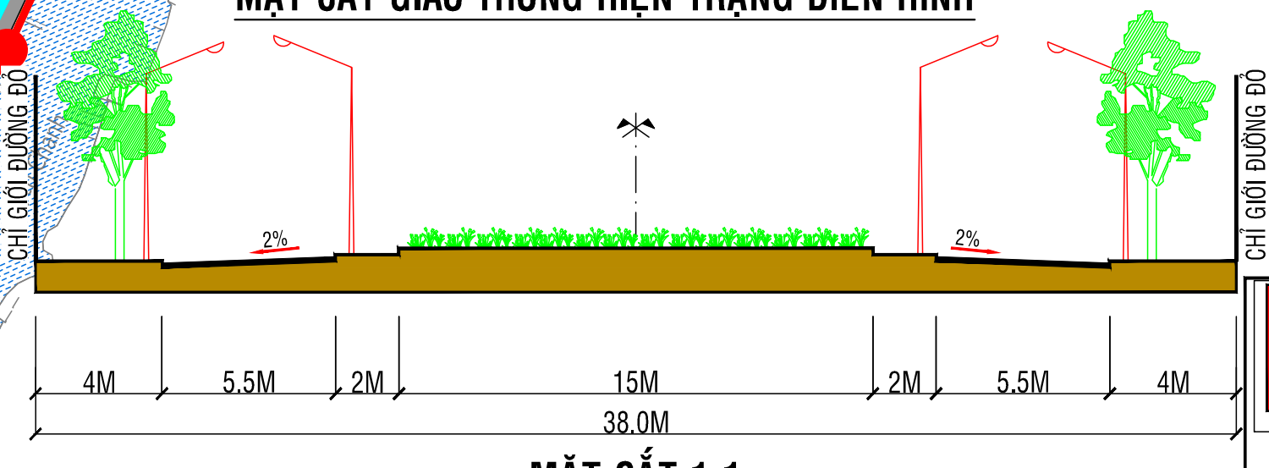

MẶT CẮT 1-1

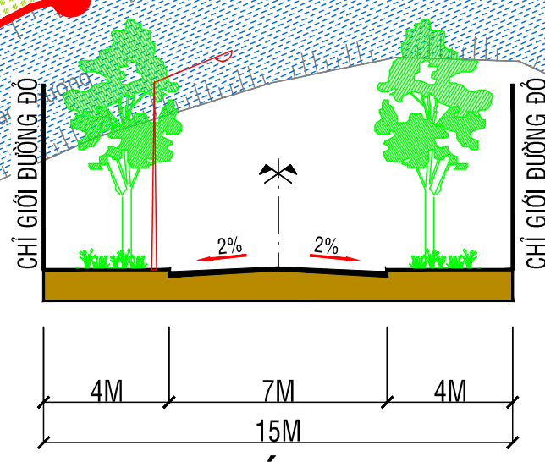

MẶT CẮT 2-2

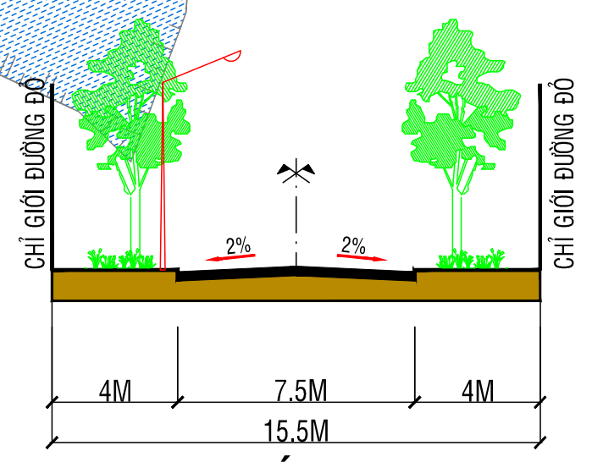

MẶT CẮT 3-3

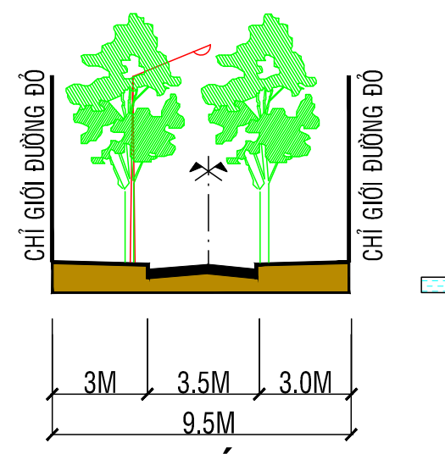

MẶT CẮT 4-4

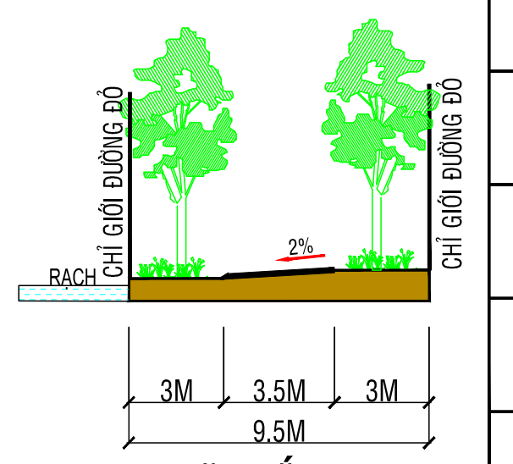

MẶT CẮT 5-5

TRƯỜNG ĐẠI HỌC KIẾN TRÚC THÀNH PHỐ HỒ CHÍ MINH
KHOA KỸ THUẬT ĐÔ THỊ
ĐỒ ÁN TỐT NGHIỆP KỸ SƯ KỸ THUẬT CƠ SỞ HẠ TẦNG KHÓA KD20

TÊN ĐỀ TÀI: QUY HOẠCH HỆ THỐNG HẠ TẦNG KỸ THUẬT TỶ LỆ 1/2000 KHU DÂN CƯ RẠCH CHANH, XÃ MỸ TRÀ, THÀNH PHỐ CAO LÃNH, TỈNH ĐỒNG THÁP

GVHD CHÍNH	ThS. ĐINH NGỌC SANG	CHỮ KÝ:		
GVHD CTN	ThS. TRẦN MINH ANH	CHỮ KÝ:		
GVHD GT-SN	TS. NGUYỄN ĐÌNH NÊN	CHỮ KÝ:		
SVTH	NGUYỄN QUANG ĐẠI	MSSV: 20521000971	HOÀN THÀNH: ---/---/-----	01 13